

04

Road-facing
shops

03

Flexible homes
on each upper floor

04

Parking bays
below road level

Independent stair
and passenger lift.

Parking access assumed from
the footpath side.



Architectural visualization of the proposed concept. Materials, surroundings and landscaping are indicative; the dimensioned plans define the layout.

EXPLORE THE FURNISHED 3D WALKTHROUGH

Click here to open the model and move between floors and rooms ↗



bhaderwah-house-walkthrough.faisal90.chatgpt.site




01 / SITE INTELLIGENCE

The site sets the geometry

Boundary dimensions are taken from SITE PLAN-2(1).pdf. The reference building layout has not been reused.

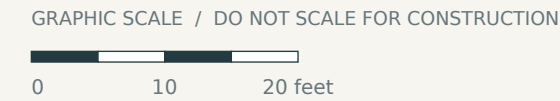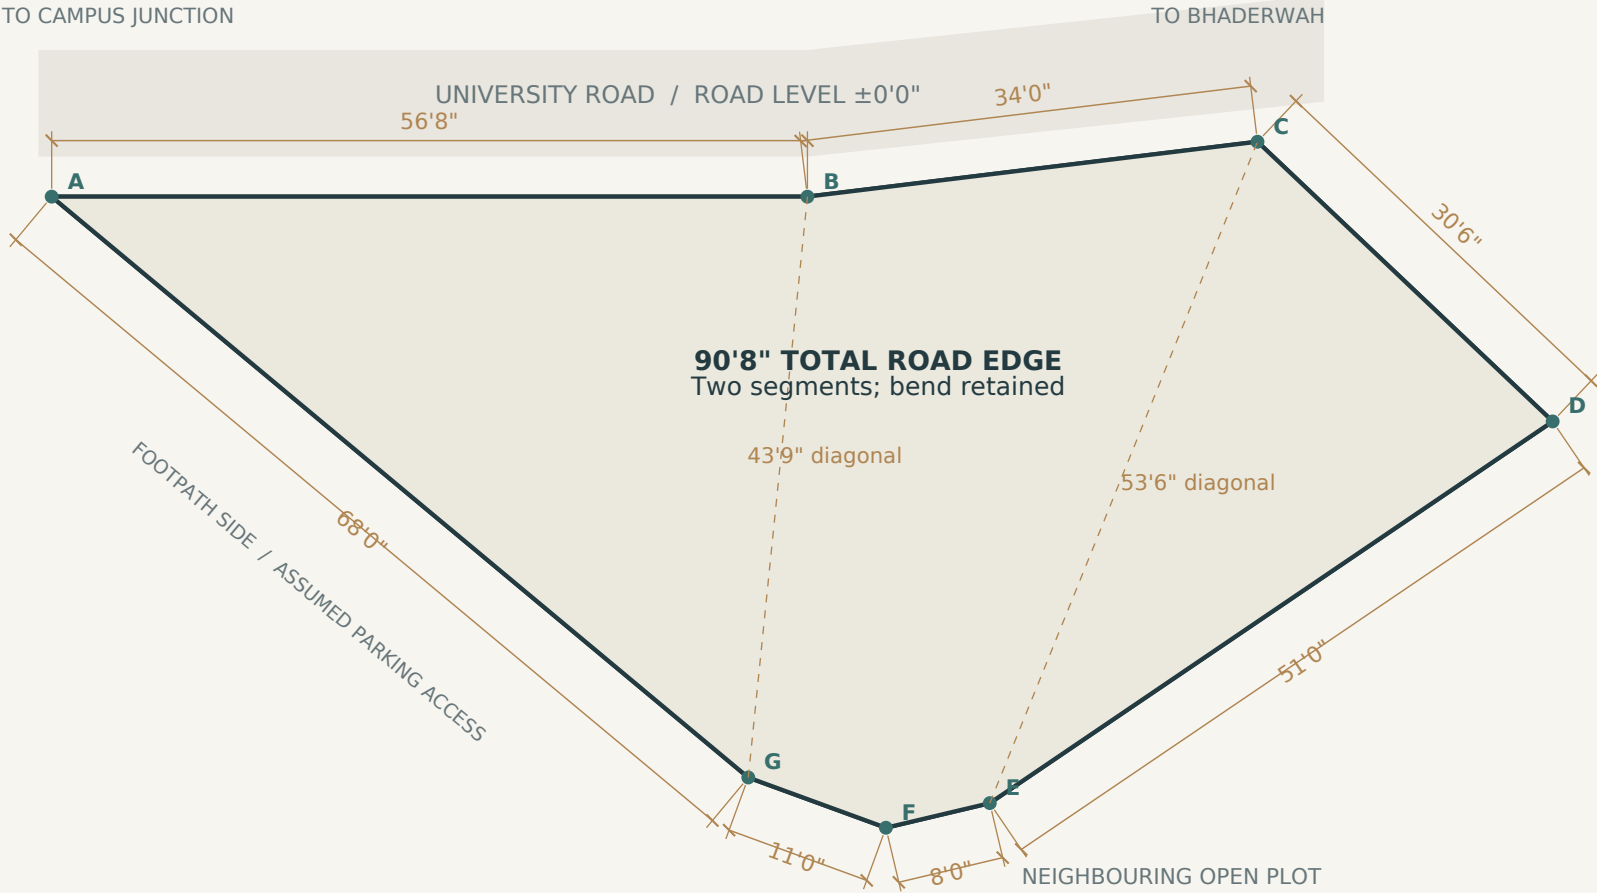

CLIENT-SUPPLIED GOOGLE EARTH CONTEXT

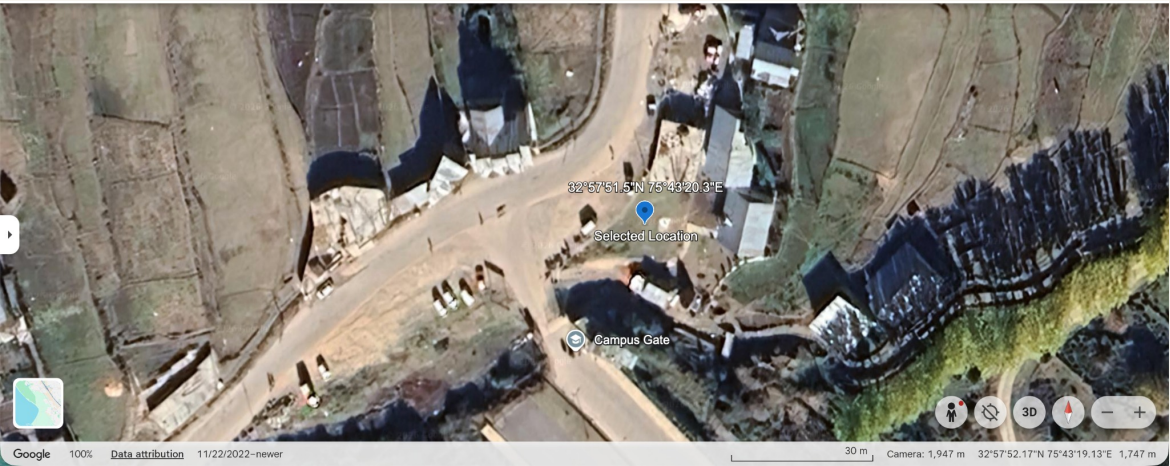

Approximate pin: 32.964308 N, 75.722306 E.
Satellite context locates the campus approach; it is not a parcel survey or a source of design levels.

A Separate arrivals

Pedestrian entry remains on University Road. Vehicle entry and exit are assumed from the footpath side at parking level. Approach geometry is outside this concept update.

B Relative levels

Road datum: $\pm 0'0''$. Existing plot: approximately -6'7", based on the client statement. No contour survey or verified spot levels were supplied.

C Orientation

Floor plans are rotated to place the long road segment at the top. True bearings are not supplied; no surveyed north arrow is implied.

Source dimensions are preserved as supplied. The vector outline has been reconciled to these dimensions; a new cadastral or topographic survey has not been performed.


02 / LOWER GROUND • PROPOSED FFL -10'0"

Parking below the road-level slab

Four parking bays are shown beneath the raised commercial floor. Arrival is assumed from the footpath side.

TO CAMPUS JUNCTION

TO BHADERWAH

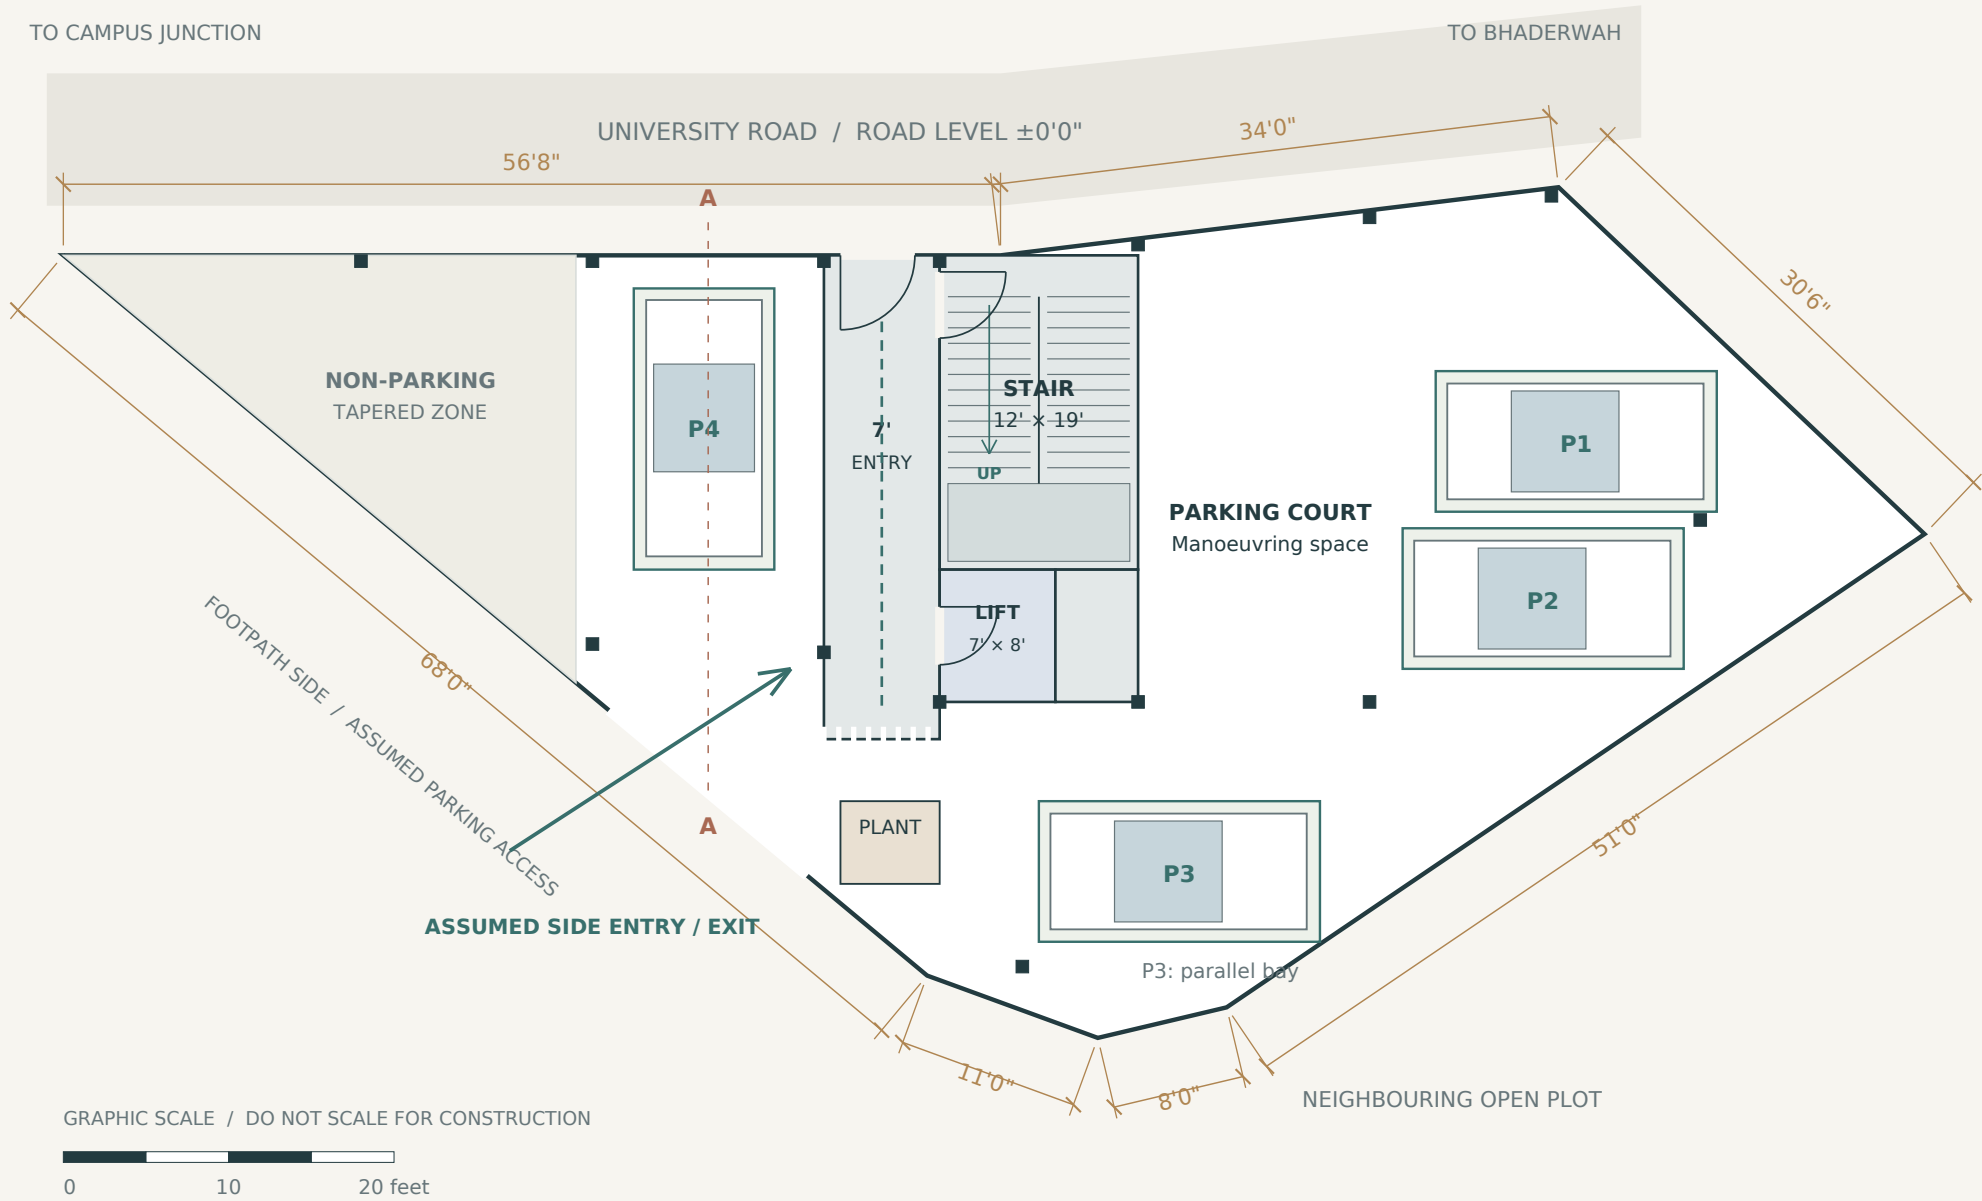

01 Four parking bays

Each bay is 8'6" × 17'0". The former vehicle-lift reservation now provides an ordinary parking bay.

02 Footpath-side access

Vehicle entry and exit are assumed at the lower level, as requested. No ramp or approach geometry is designed in this update.

03 Independent pedestrian route

The stair and passenger lift stay in the same location. Parking users reach the upper floors through the shared core, independently of all shops.

04 Road-level slab

The retail floor stays flush with the road. The parking datum is -10'0", providing space for the frame and an indicative 8'6" clear parking height.


What changed. The vehicle lift and its pit have been removed. The road-facing bay above P4 becomes a fourth shop. The apartment layout and independent pedestrian entrance remain aligned with the earlier concept.

Side access is a client assumption for this concept. Parking spaces are indicative; detailed circulation and statutory parking assessment follow at the next stage. Column positions are indicative only.

03 / ROAD LEVEL • PROPOSED FFL ±0'0"

A clear commercial address

Four visible tenancies and a dedicated entrance to the upper floors. Retail fit-outs remain flexible.

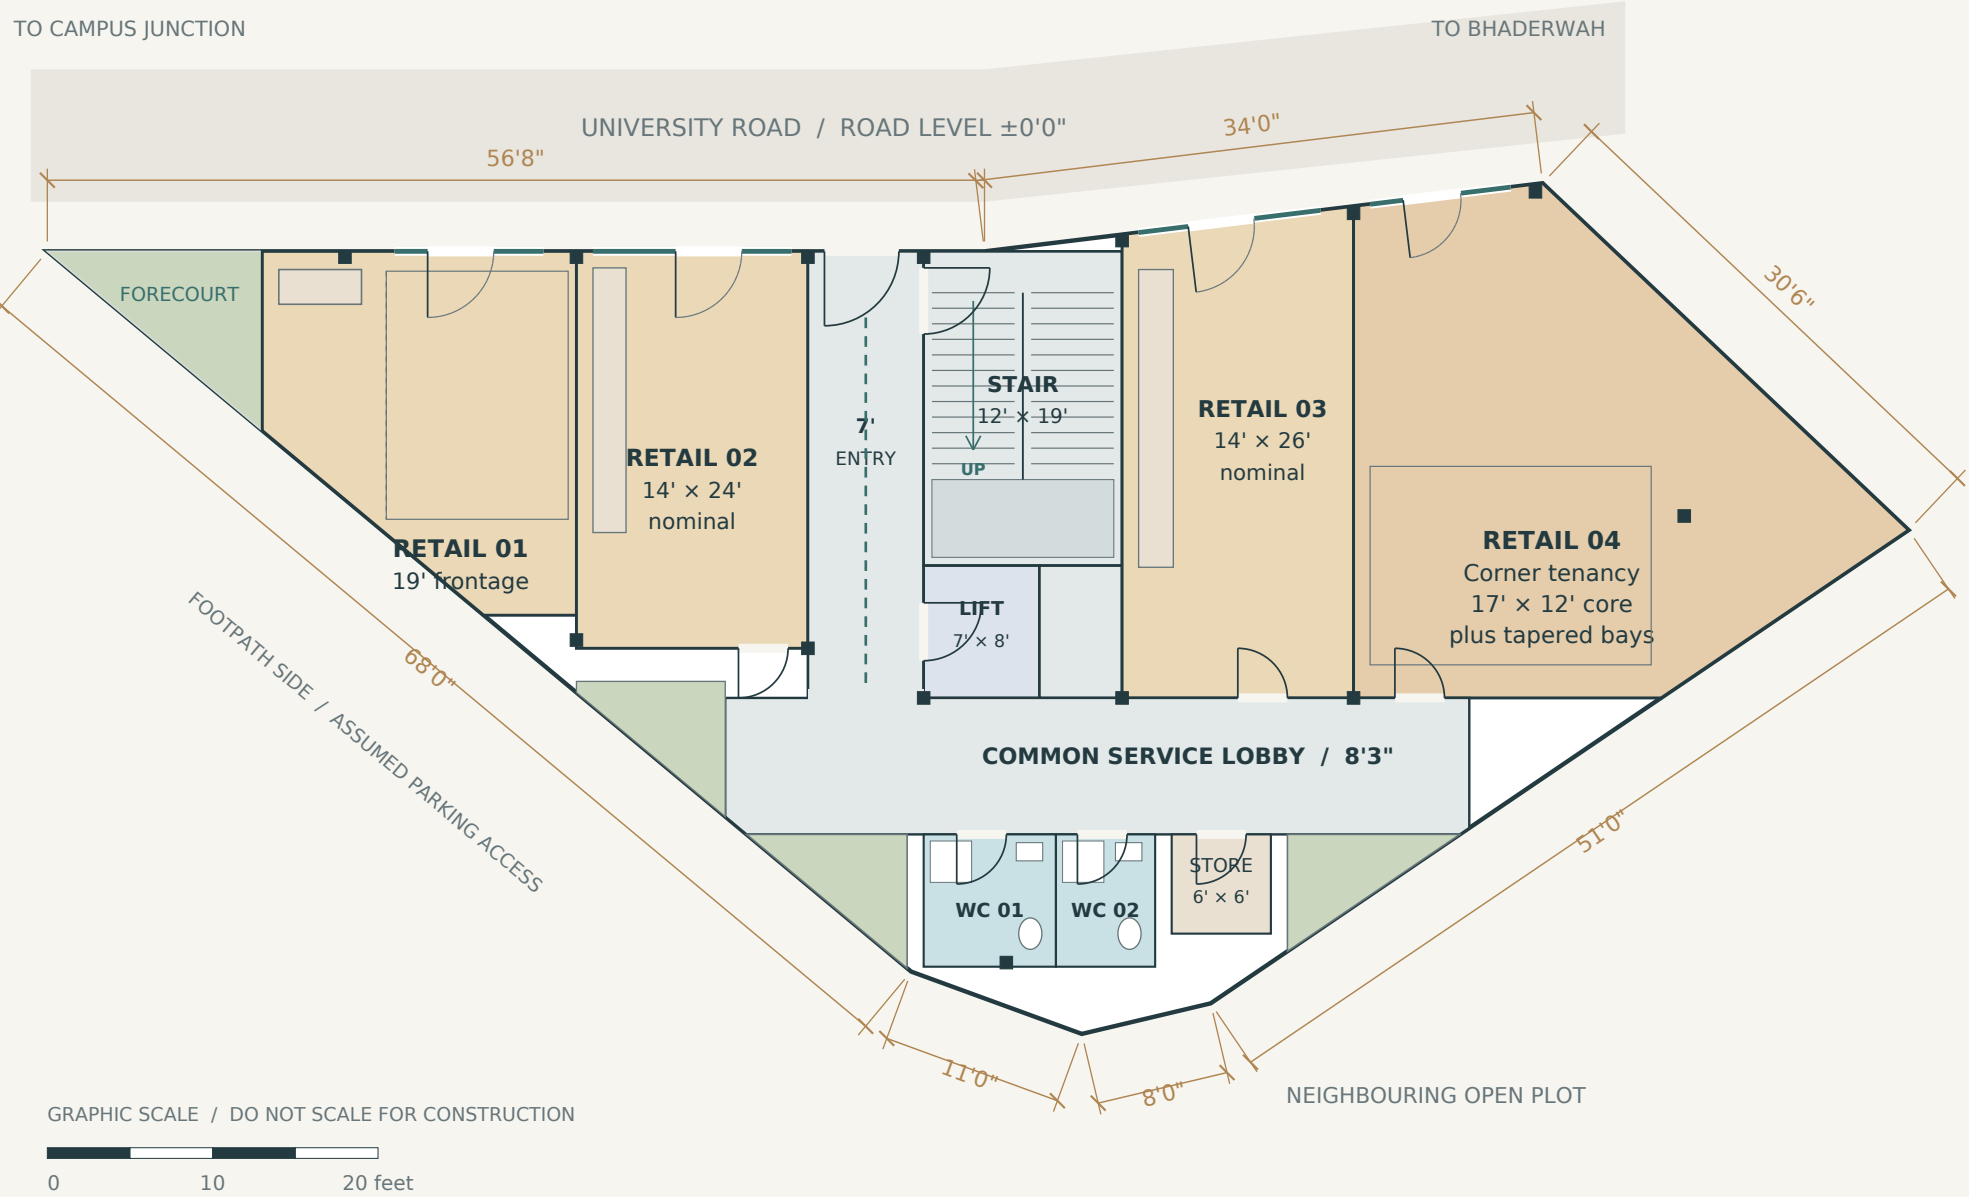

01 Retail 01 / campus edge

19' road frontage with a tapered plan. An 11' x 15' rectangular fit-out zone supports a compact café, stationery or convenience offer, subject to tenant demand.

02 Retail 02 + 03 / regular bays

Retail 02 is 14' x 24'; Retail 03 is 14' x 26' nominally. The new second shop occupies the former vehicle-lift bay.

03 Retail 04 / corner

The actual second road segment is retained. A 17' x 12' rectangular core sits within the taper. Furniture, storage and display use the wider end of the plot.

04 Shared support

Two common toilets and a store are reached from the dedicated lobby. Retail 01 uses the road-facing lobby entrance; all four shops have their own road entrance.


Commercial approach. Offer four legible addresses and adaptable fit-outs. Tenant selection, frontage permissions and achieved rents should guide final subdivisions; no rental-income forecast is assumed.

Internal sizes are nominal planning dimensions. The exact clear fit-out sizes depend on wall build-ups, columns and services. Common toilet layout and fixture count require detailed accessibility and occupancy checks.

04 / FIRST FLOOR • PROPOSED FFL +12'6"

Homes with their own front door

Two one-bedroom apartments and one studio. Every unit connects privately to its own kitchen and bathroom.

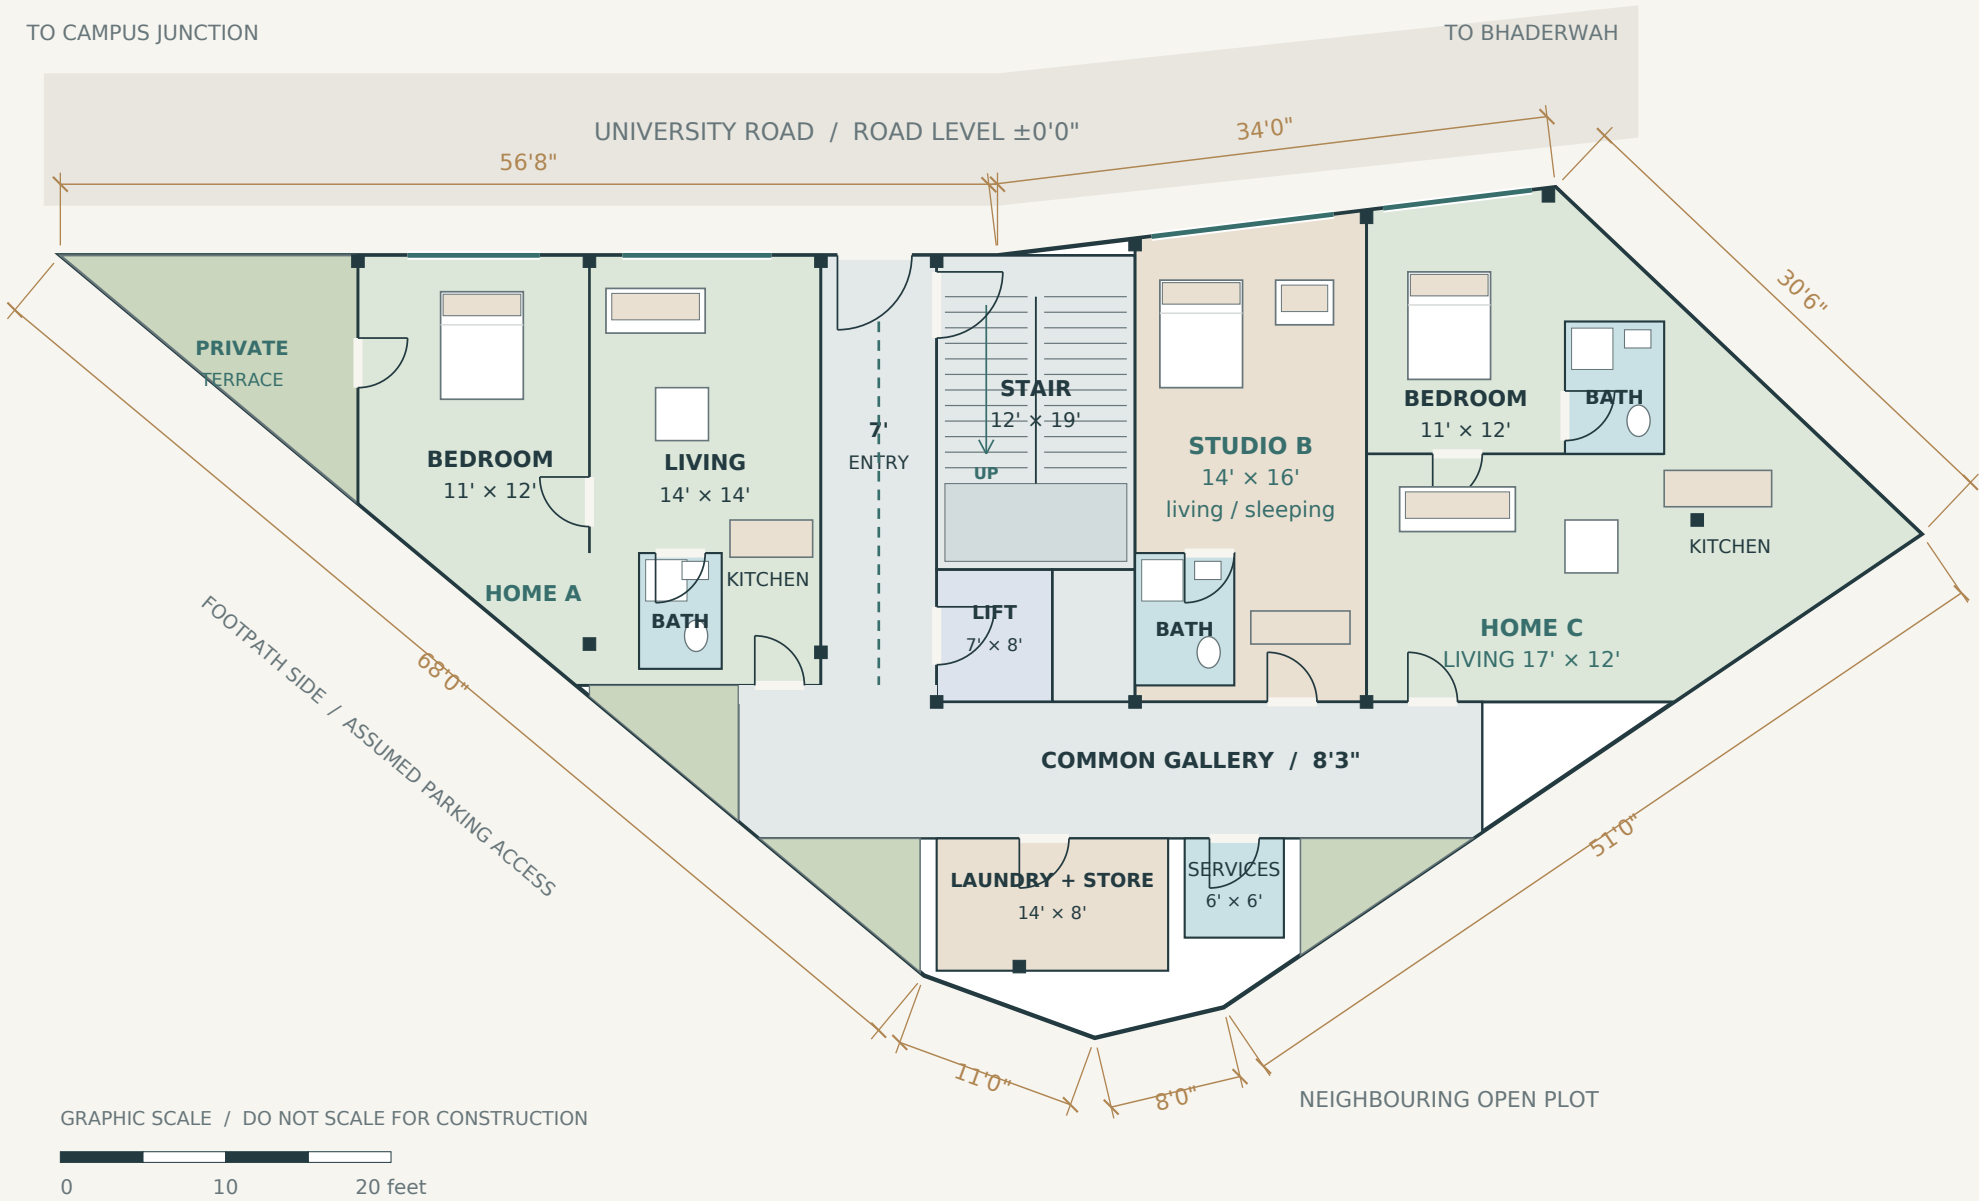

Daylight strategy. Main sleeping/living spaces take windows directly from the road frontage. Rear planting strips and service ventilation are within the working envelope; the design does not rely on future public access across neighbouring land.

01 Home A / one bedroom

Bedroom 11' x 12'; living core 14' x 14'; bath 5' x 7'. The tapered campus end becomes a private terrace and useful storage, rather than a narrow sleeping space.

02 Studio B

A 14' x 16' living/sleeping core, a 6' x 8' bath and a kitchenette. One entrance from the gallery; direct road-facing windows.

03 Home C / one bedroom

Bedroom 11' x 12'; living core 17' x 12'; bath 6' x 8'. The bedroom connects internally to the living room. The irregular end accommodates kitchen and built-in storage.

04 A consistent service core

The stair, passenger lift and wet zones stay aligned above the commercial floor. The rear gallery reaches the common laundry and service room.

Dimensions describe nominal room cores, not the full area of irregular units. Terrace guards, window ventilation, sound separation, protected escape and the lawful building envelope remain part of the next design stage.


05 / SECOND FLOOR • PROPOSED FFL +23'0"

One layout, two operating choices

The same three-unit arrangement can support long-term lets or self-contained serviced stays, subject to the approved use.

TO CAMPUS JUNCTION

TO BHADERWAH

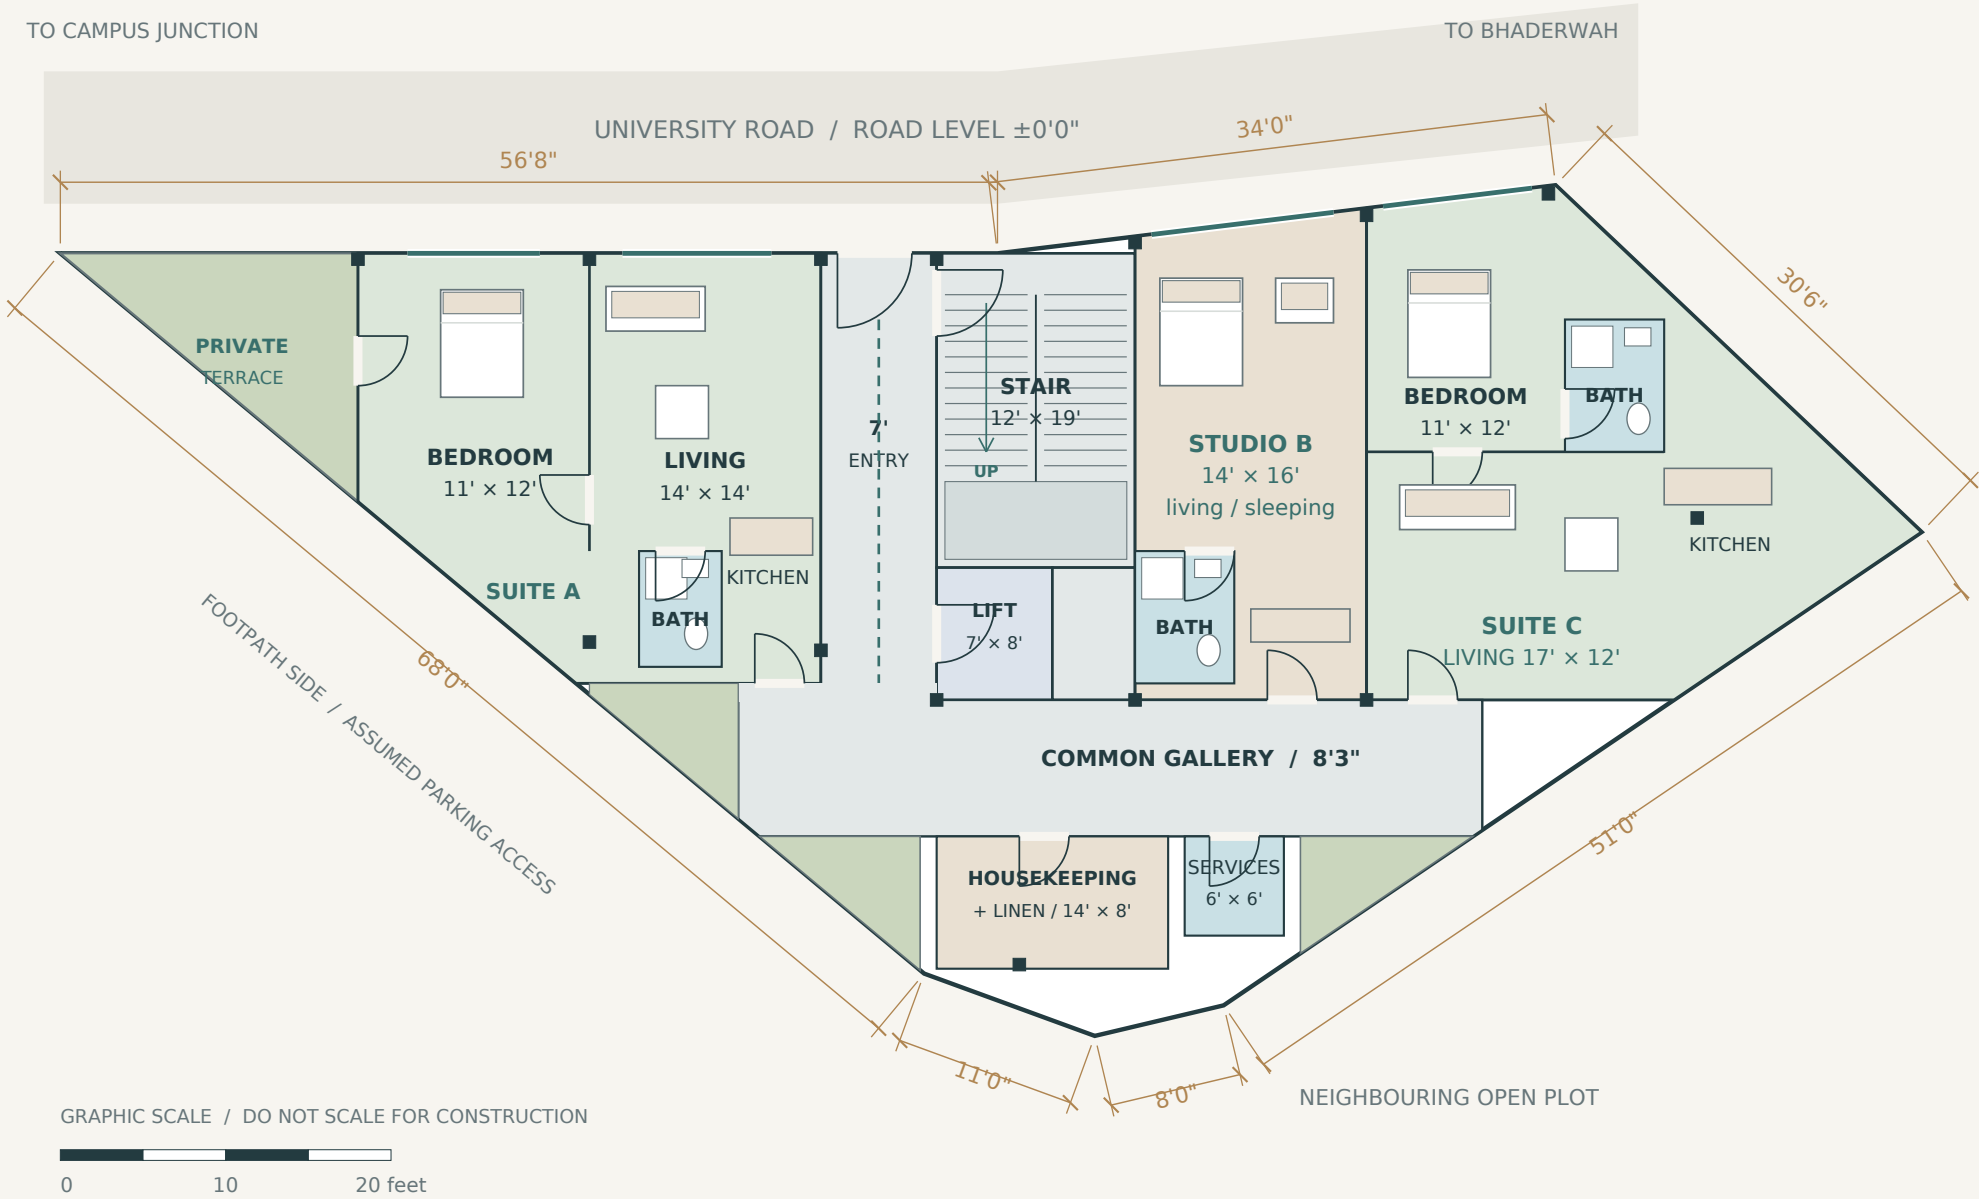

01 Suite A / one bedroom

A separate bedroom and living room support a couple or a small family. The living room can accept a sofa bed after checking final clearances and permitted occupancy.

02 Studio B

A compact self-contained stay with a kitchen point and private bathroom. Suitable for an individual or couple, subject to operating requirements.

03 Suite C / one bedroom

A larger living room and a private bedroom provide a family-oriented option. The kitchenette sits in the corner extension, keeping the room core regular.

04 Flexible management

Housekeeping and linen use the common rear room. Access control and a small host/check-in point can be integrated with the arrival lobby without blocking the escape route.

Owner choice. Fit out as ordinary rentals first, or furnish for serviced stays once demand and management arrangements are established. Physical adaptability does not itself grant a change-of-use approval.

No occupancy, room-rate or revenue projections are assumed. Confirm the local accommodation classification, fire strategy, parking provision and operating permissions before selecting short-stay use.


06 / SECTION + ARCHITECTURAL EXPRESSION

The road and the building work together

Relative levels are a design proposal based on the stated road-to-plot difference. Final levels require a measured topographic survey.

A-A / SECTION THROUGH RETAIL 02

Cut through Retail 02 and parking; plot depth here is approximately 32'6".

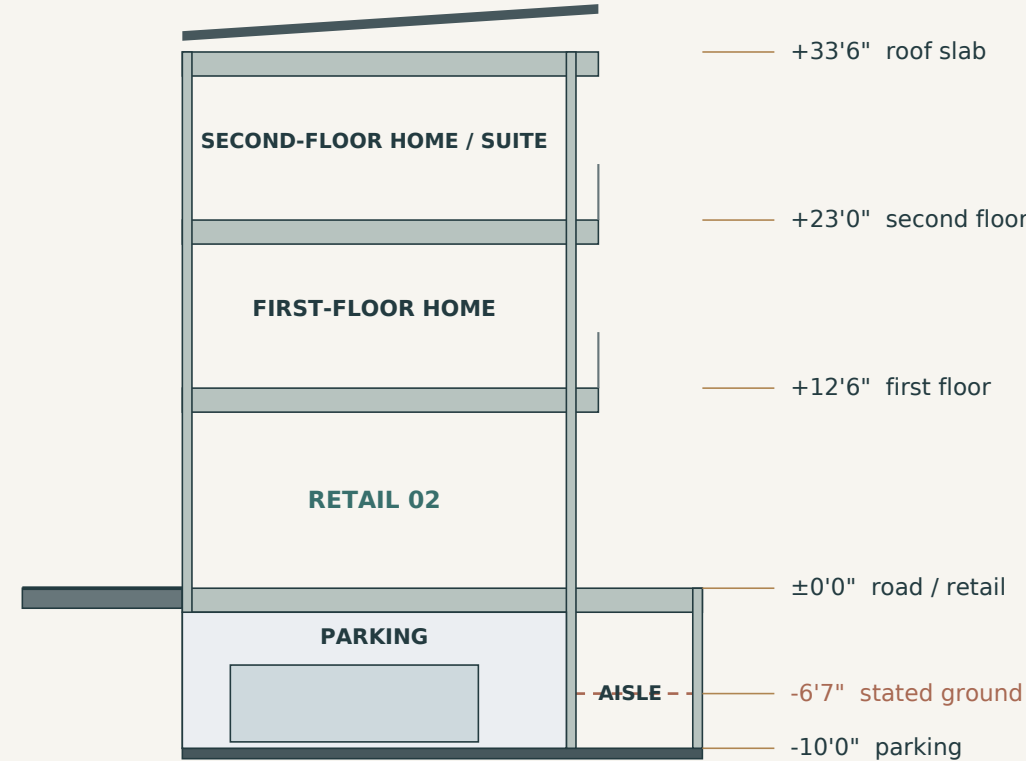


Side parking access is outside the section plane.

The proposed parking floor is 3'5" below the stated existing ground. A 1'6" structural zone below road level leaves an indicative 8'6" parking clearance. These are coordination allowances, not structural member designs.

B-B / UNFOLDED ROAD ELEVATION

Frontage bend retained in the plans; elevation unfolded for clarity.

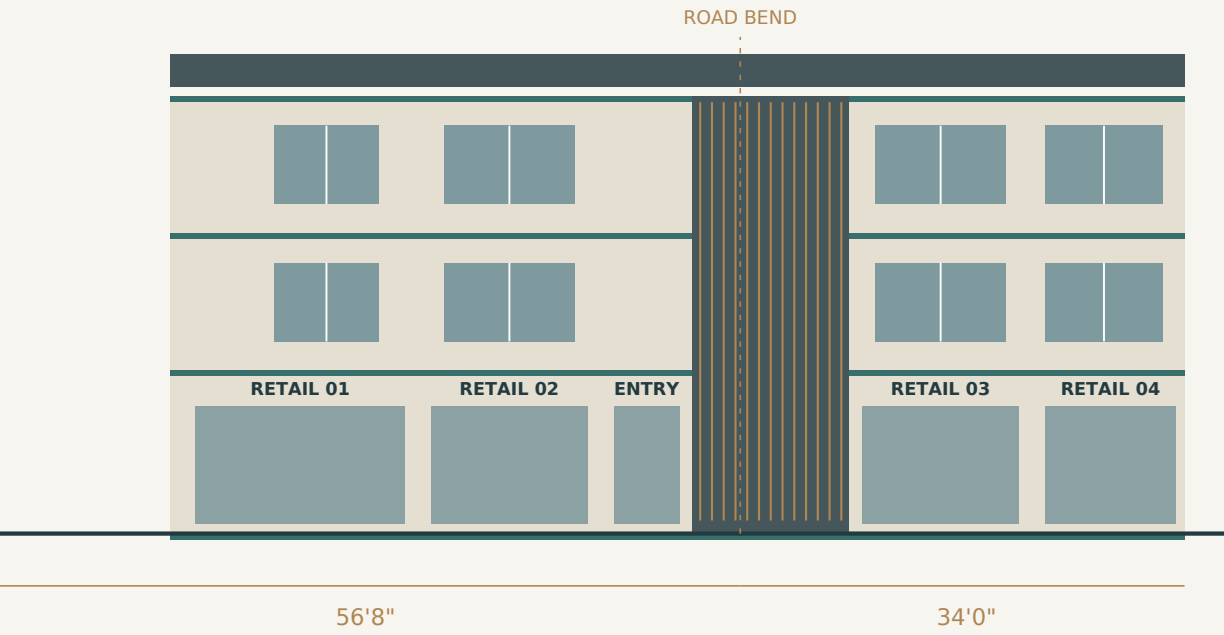

Architectural character. Warm mineral-coloured walls, a stone-toned lower plinth, restrained bronze/wood-tone screens and a charcoal standing-seam roof. Recessed shopfronts keep canopies within the working boundary.



Roof pitch, drainage, snow/seismic design, façade materials, waterproofing and the impact of adjoining construction require local engineering. No Google Earth spot level is used as a design datum.

07 / ACCOMMODATION SCHEDULE + DESIGN BASIS

A coordinated brief for the next stage

Updated family concept using the supplied site dimensions, with side-access parking and four road-facing shops.

SPACE / USE	PROPOSED DIMENSIONS	DESIGN INTENT
Road level / Retail 01	19' frontage; 11' × 15' fit-out core	Tapered campus-end tenancy; independent road-facing entrance.
Road level / Retail 02 + 03	14' × 24'; 14' × 26'	Two regular shops; the former vehicle-lift bay is now Retail 02.
Road level / Retail 04	17' × 12' rectangular core	Corner tenancy within the actual 34' road segment; tapered parts support fit-out.
Each upper floor / Home or Suite A	Bed 11' × 12'; living 14' × 14'	One bedroom, kitchenette and 5' × 7' bathroom; private tapered terrace.
Each upper floor / Studio B	Living/sleeping 14' × 16'	Kitchenette and 6' × 8' bathroom; one entrance from the shared gallery.
Each upper floor / Home or Suite C	Bed 11' × 12'; living 17' × 12'	One bedroom, kitchenette and 6' × 8' bathroom; internal room connection.
Lower ground / Parking target	4 bays, each 8'6" × 17'0"	Footpath-side access assumed; approach geometry is outside this concept.

TO DEVELOP BEFORE SCHEMATIC DESIGN

Survey + permissions. Confirm legal boundary, bearings, road width/reservation, approved land use, setbacks, floor-area/height controls and levels along the entire frontage. The drawn envelope is a feasibility assumption, not a zero-setback approval.	Access + operations. Develop the assumed footpath-side parking connection and obtain a passenger-lift layout. Confirm the allowed single-stair strategy, fire separation, travel distance and accessible routes for the chosen occupancy.
Frame + ground. Coordinate geotechnical advice, excavation support beside the raised road, retaining walls, foundations, seismic frame behaviour and parking waterproofing. Columns shown in the plans are indicative only.	Services + demand. Confirm water, sewer/outfall, power, drainage, mechanical ventilation and metering. Check actual tenant demand and short-stay permissions before fixing fit-outs or operating assumptions.
	Regulatory reference: J&K Unified Building Bye-Laws 2021; current local provisions to verify.

REFERENCE BASIS

Client-supplied SITE PLAN-2(1).pdf and AYAZ AHMED SHAIKH BHADERWAH.pdf, dated September 2026; client Google Earth screenshots and stated level difference. Prior Floor_Plans_v5 layout not adopted.